



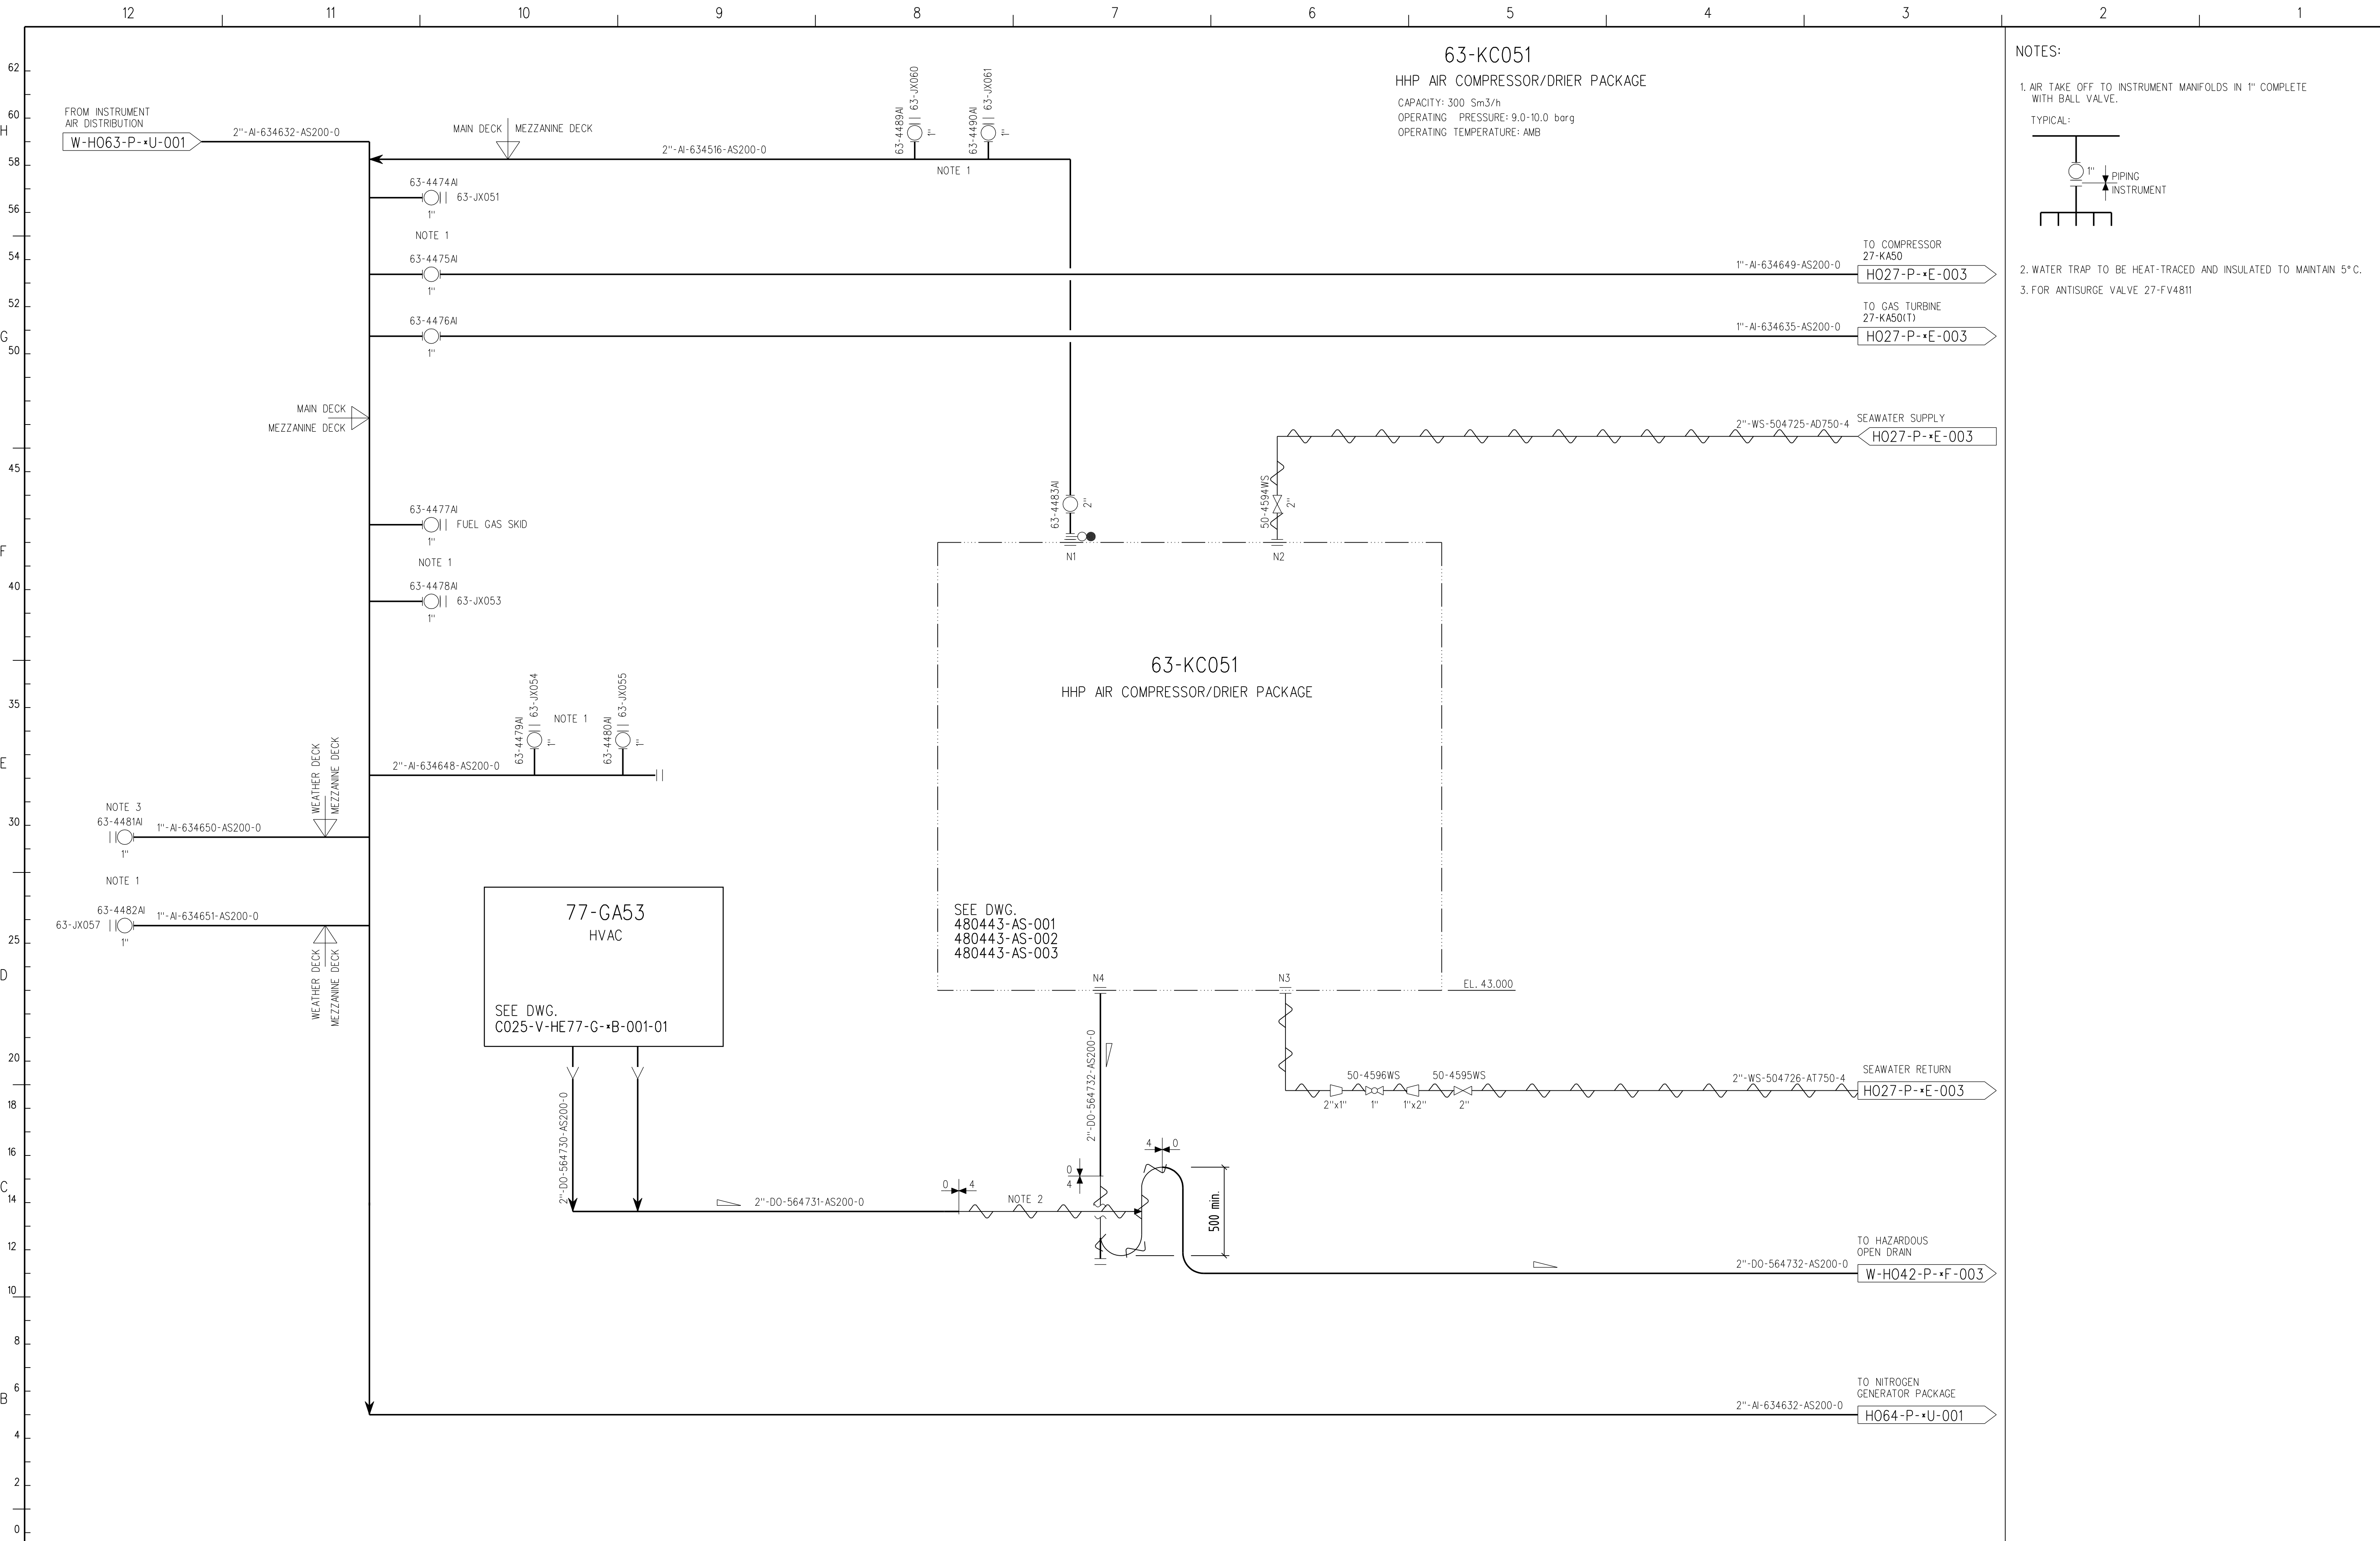

NOTES:

- 1. AIR TAKE OFF TO INSTRUMENT MANIFOLDS IN 1" COMPLETE WITH BALL VALVE.
- 2. WATER TRAP TO BE HEAT-TRACED AND INSULATED TO MAINTAIN 5°C.
- 3. FOR ANTISURGE VALVE 27-FV4811

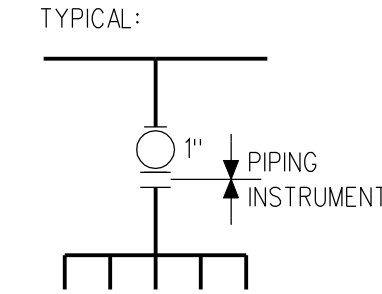

Station: UBT - MicroStation - A1	
----------------------------------	--	--	